


# Opacity Comparisons

**20110069**

<b>H P A</b>	Rooms 9	Sq. Feet: Total 2220	Size: Width 72
	Bedrooms 4	Depth 26	
<b>1st</b>	1128		
2nd	1092		
3rd			
Base			


Design, Inc.  
ARCHITECTS

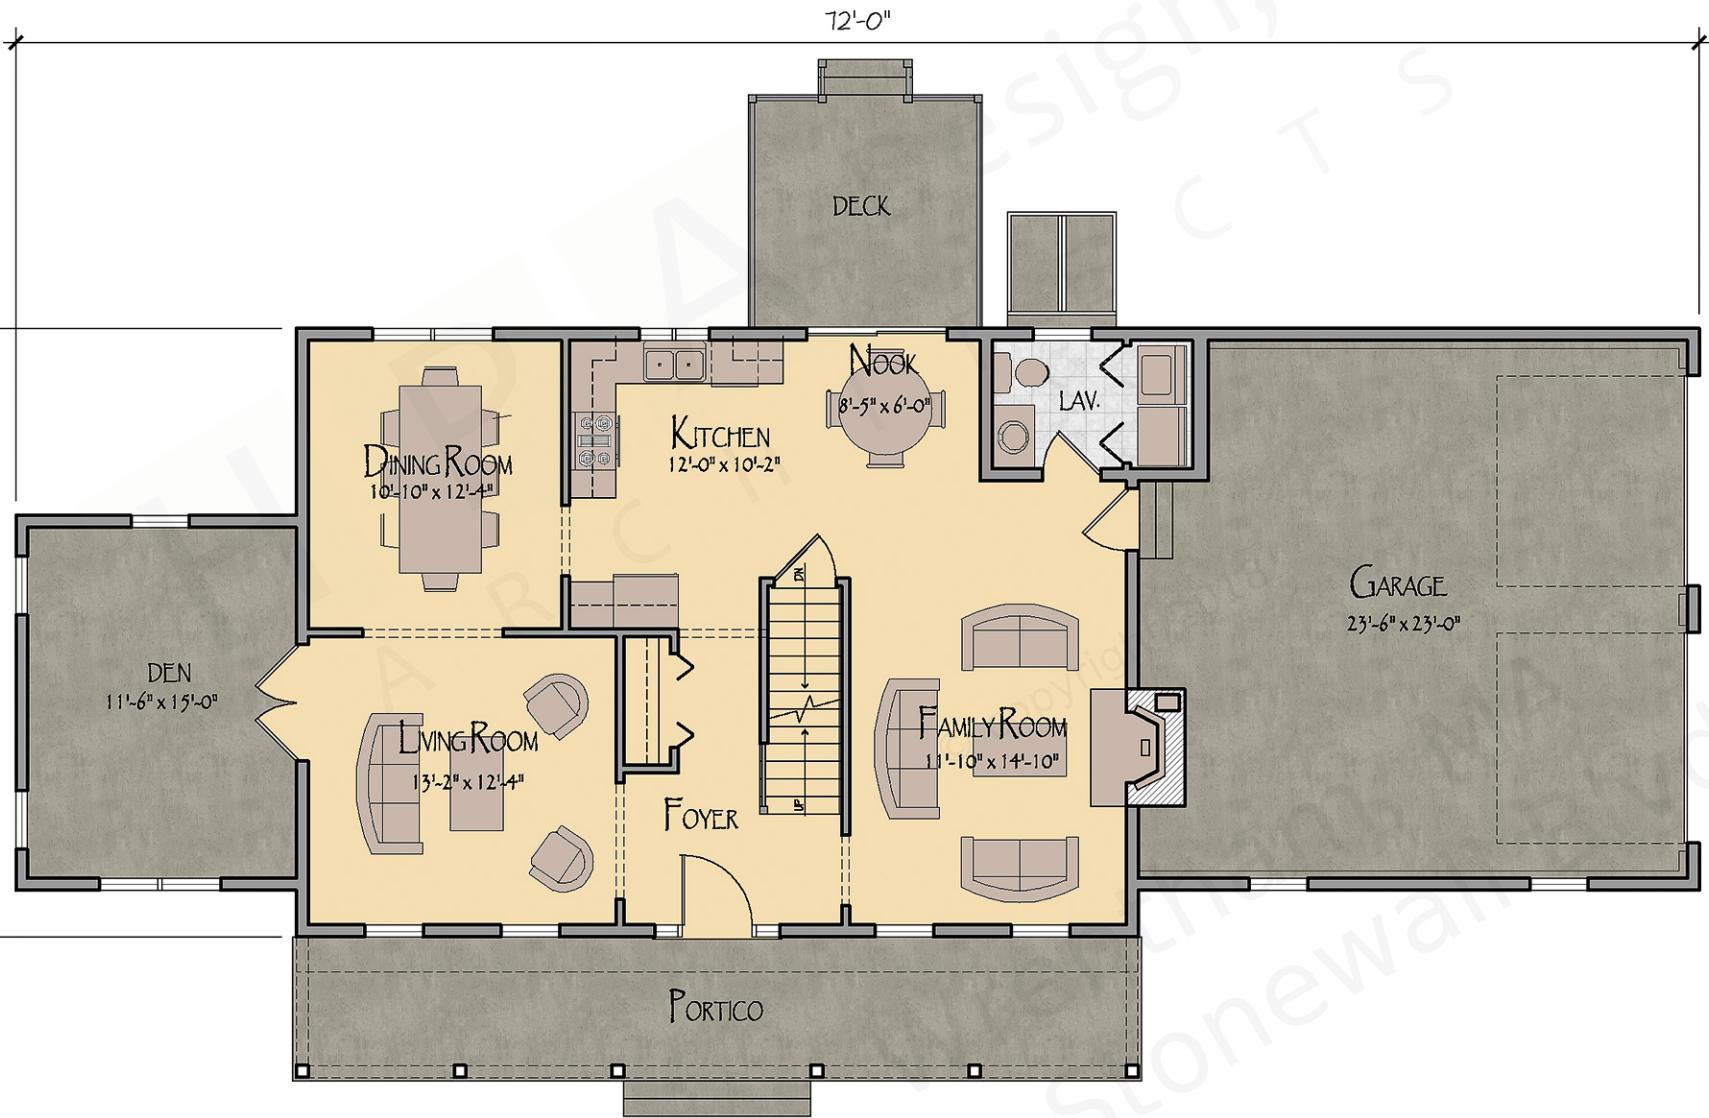

**20110069**

Rooms	9	Sq. Feet: Total	2220	Size: Width	72
<b>1st</b>	1128	Depth	26		
2nd	1092				
3rd					
Base					
H P A	Bedrooms	4			
	Baths: Full	2			
	Half	1			
	Garage Size	2			

**H P A**  
Design, Inc.  
ARCHITECTS

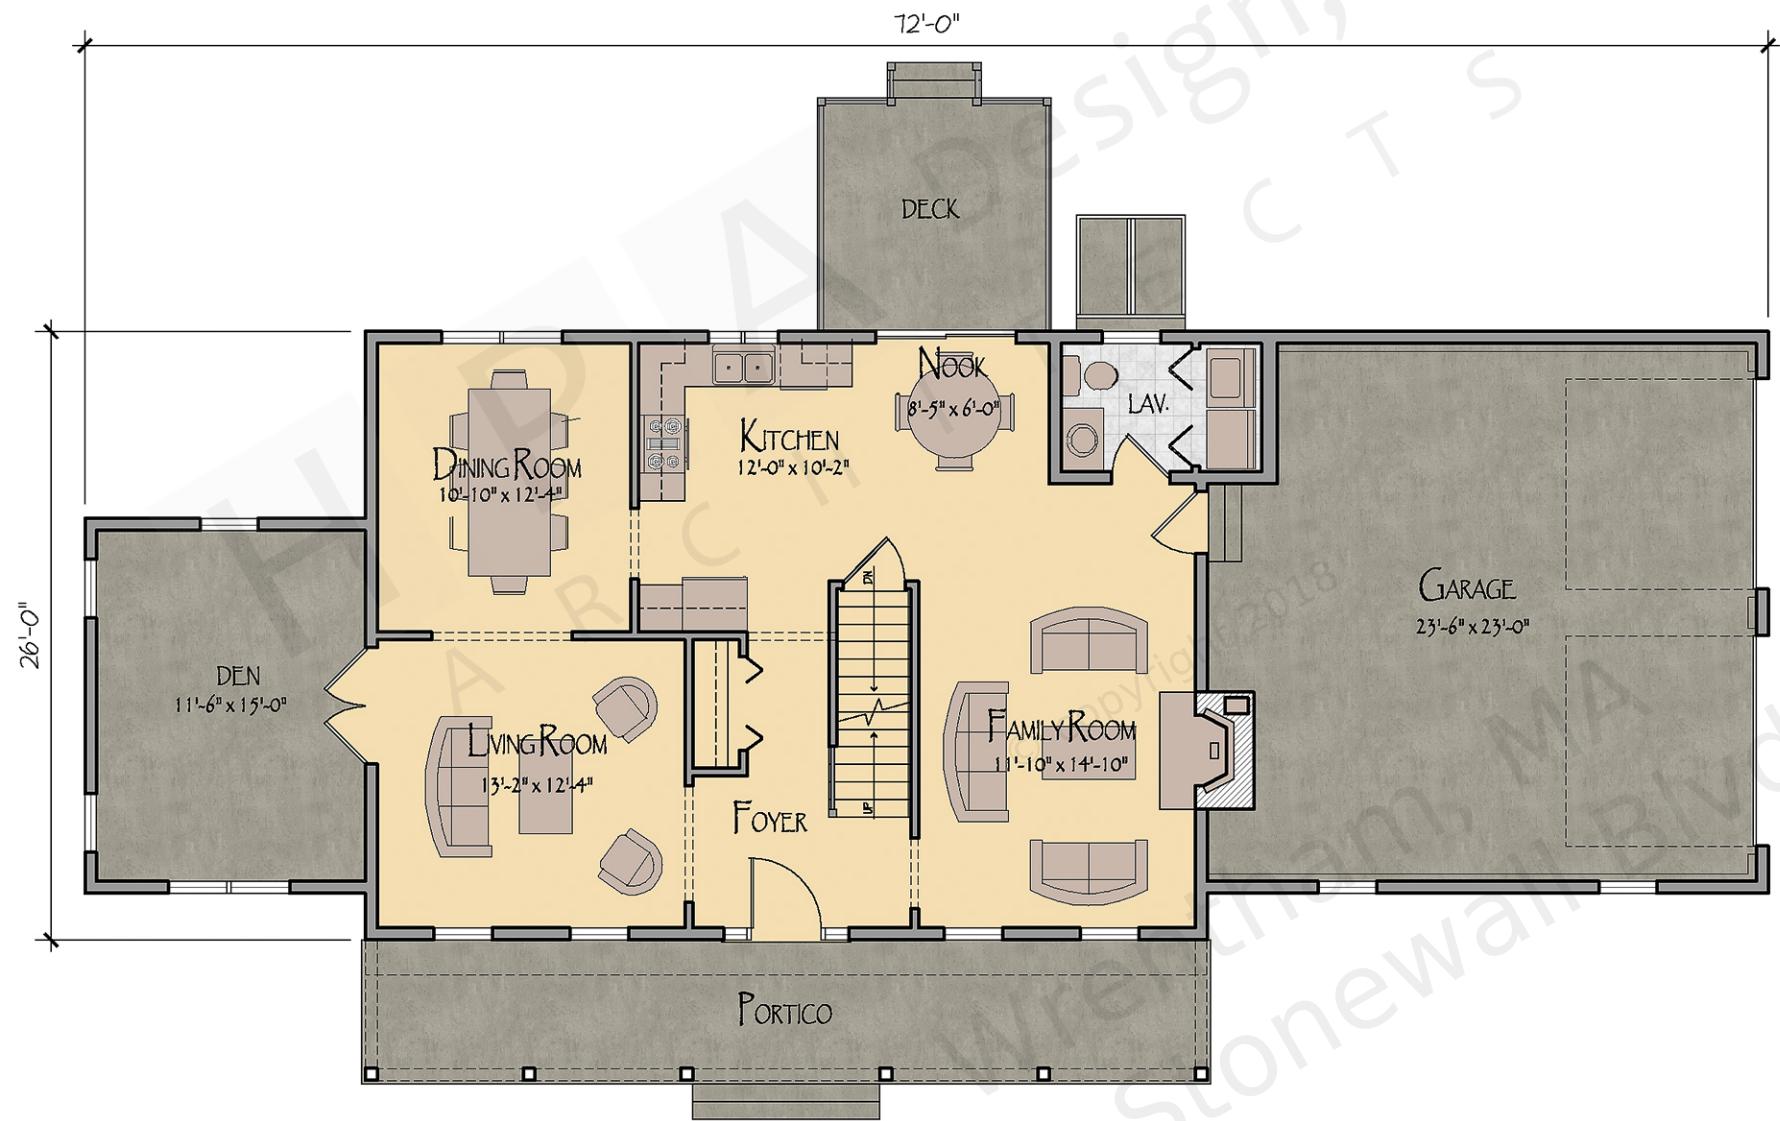


**H P A**  
Design, Inc.  
ARCHITECTS

200 Stonewall Blvd  
Wareham, MA

Rooms	9	Sq. Feet: Total	2220	Size: Width	72
Bedrooms	4	1st	1128	Depth	26
Baths: Full	2	2nd	1092		
Half	1	3rd			
Garage Size	2	Base			


<b>20110069</b>

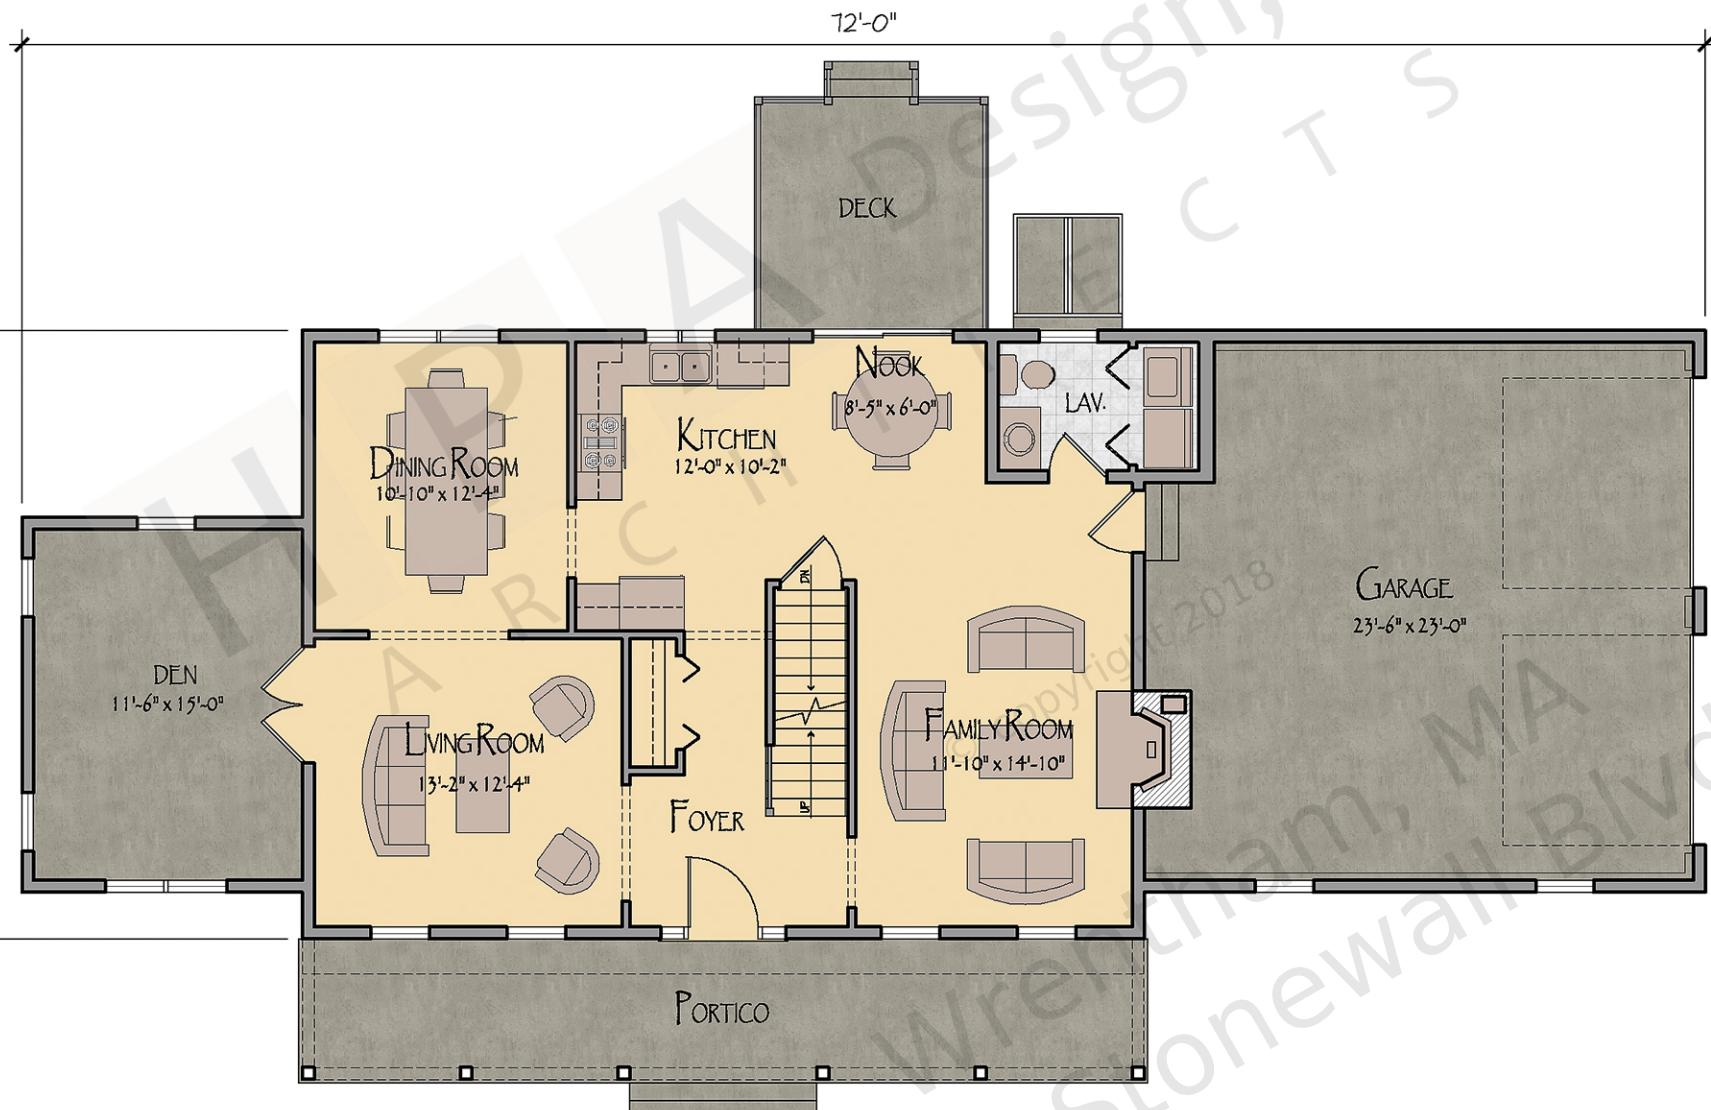

10%

**20110069**

<b>H P A</b>	Rooms 9	Sq. Feet: Total 2220	Size: Width 72
	Bedrooms 4	Depth 26	Depth 26
	Baths: Full 2		
	Half 1		
	Garage Size 2		
<b>1st</b>	1128		
<b>2nd</b>	1092		
<b>3rd</b>			
Base			

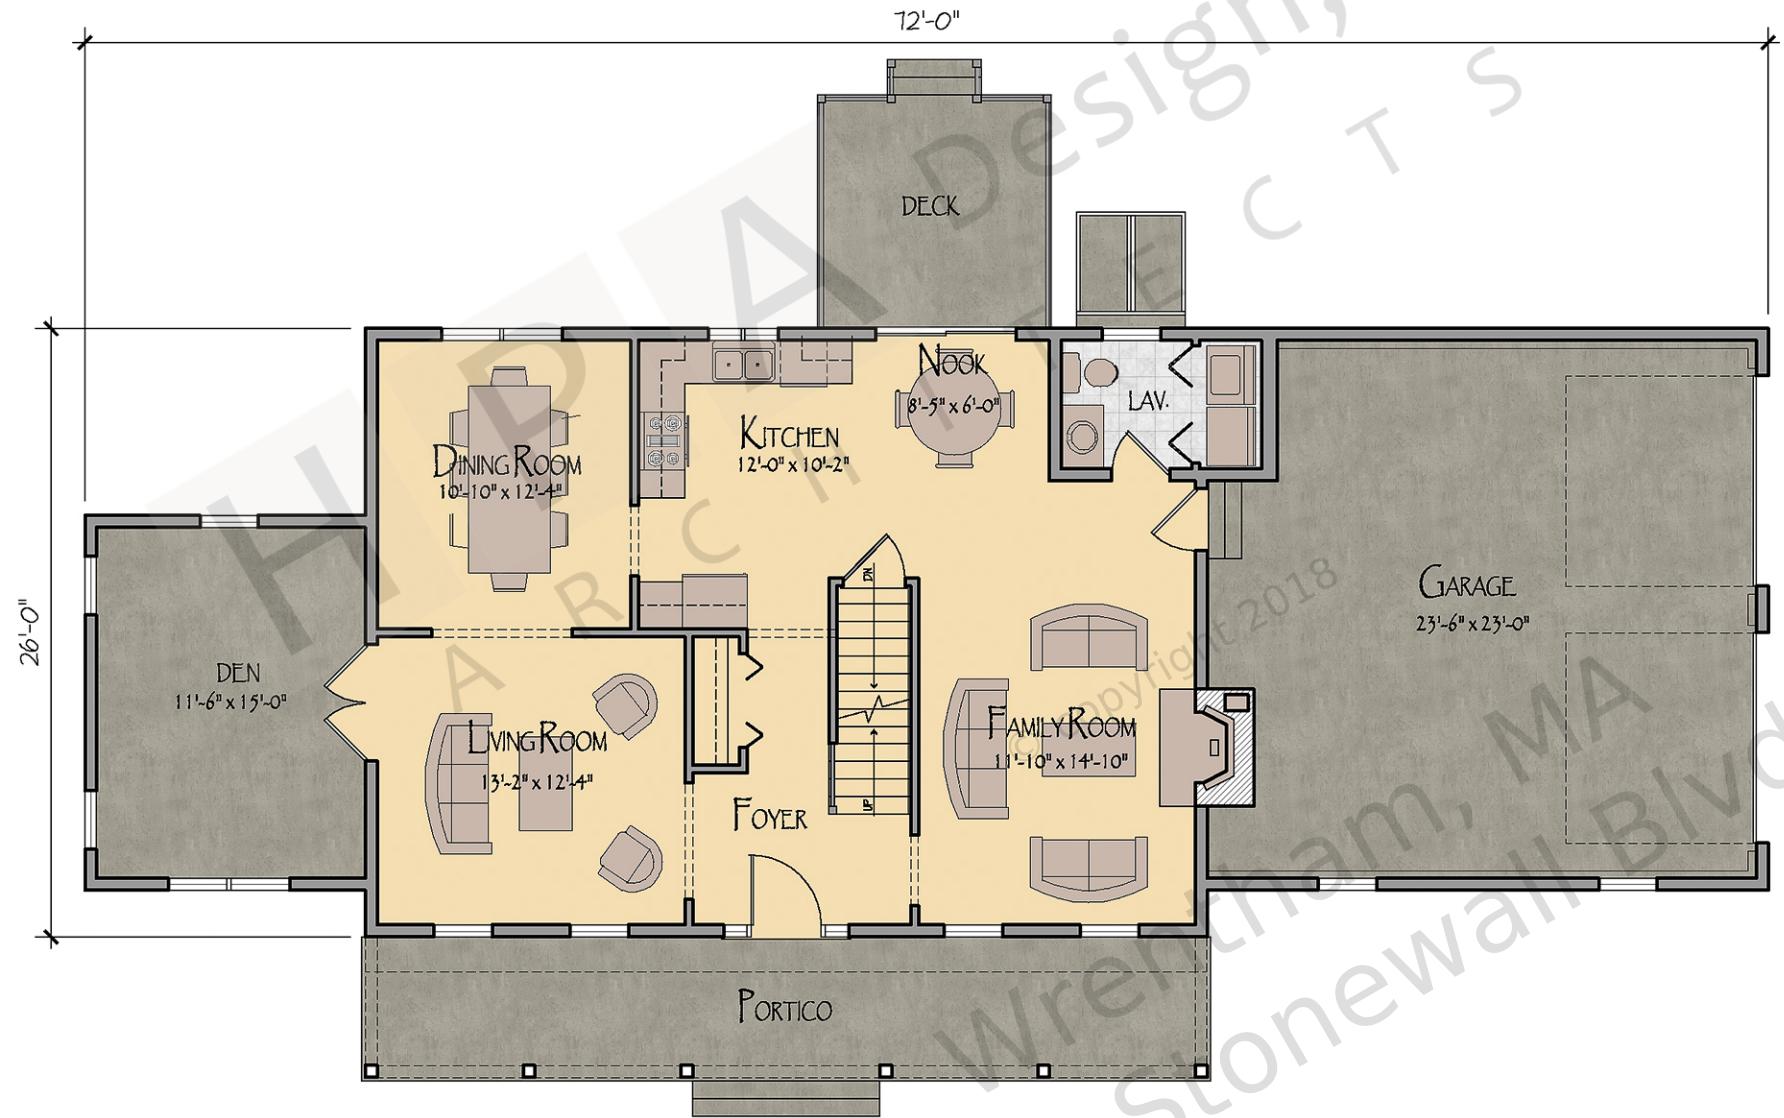


**20110069**

**H P A**  
Design, Inc.  
ARCHITECTS

16%  
200 Stonewall Blvd  
Wrentham, MA

Rooms	9	Sq. Feet: Total	2220	Size: Width	72
Bedrooms	4	1st	1128	Depth	26
Baths: Full	2	2nd	1092		
Half	1	3rd			
Garage Size	2	Base			

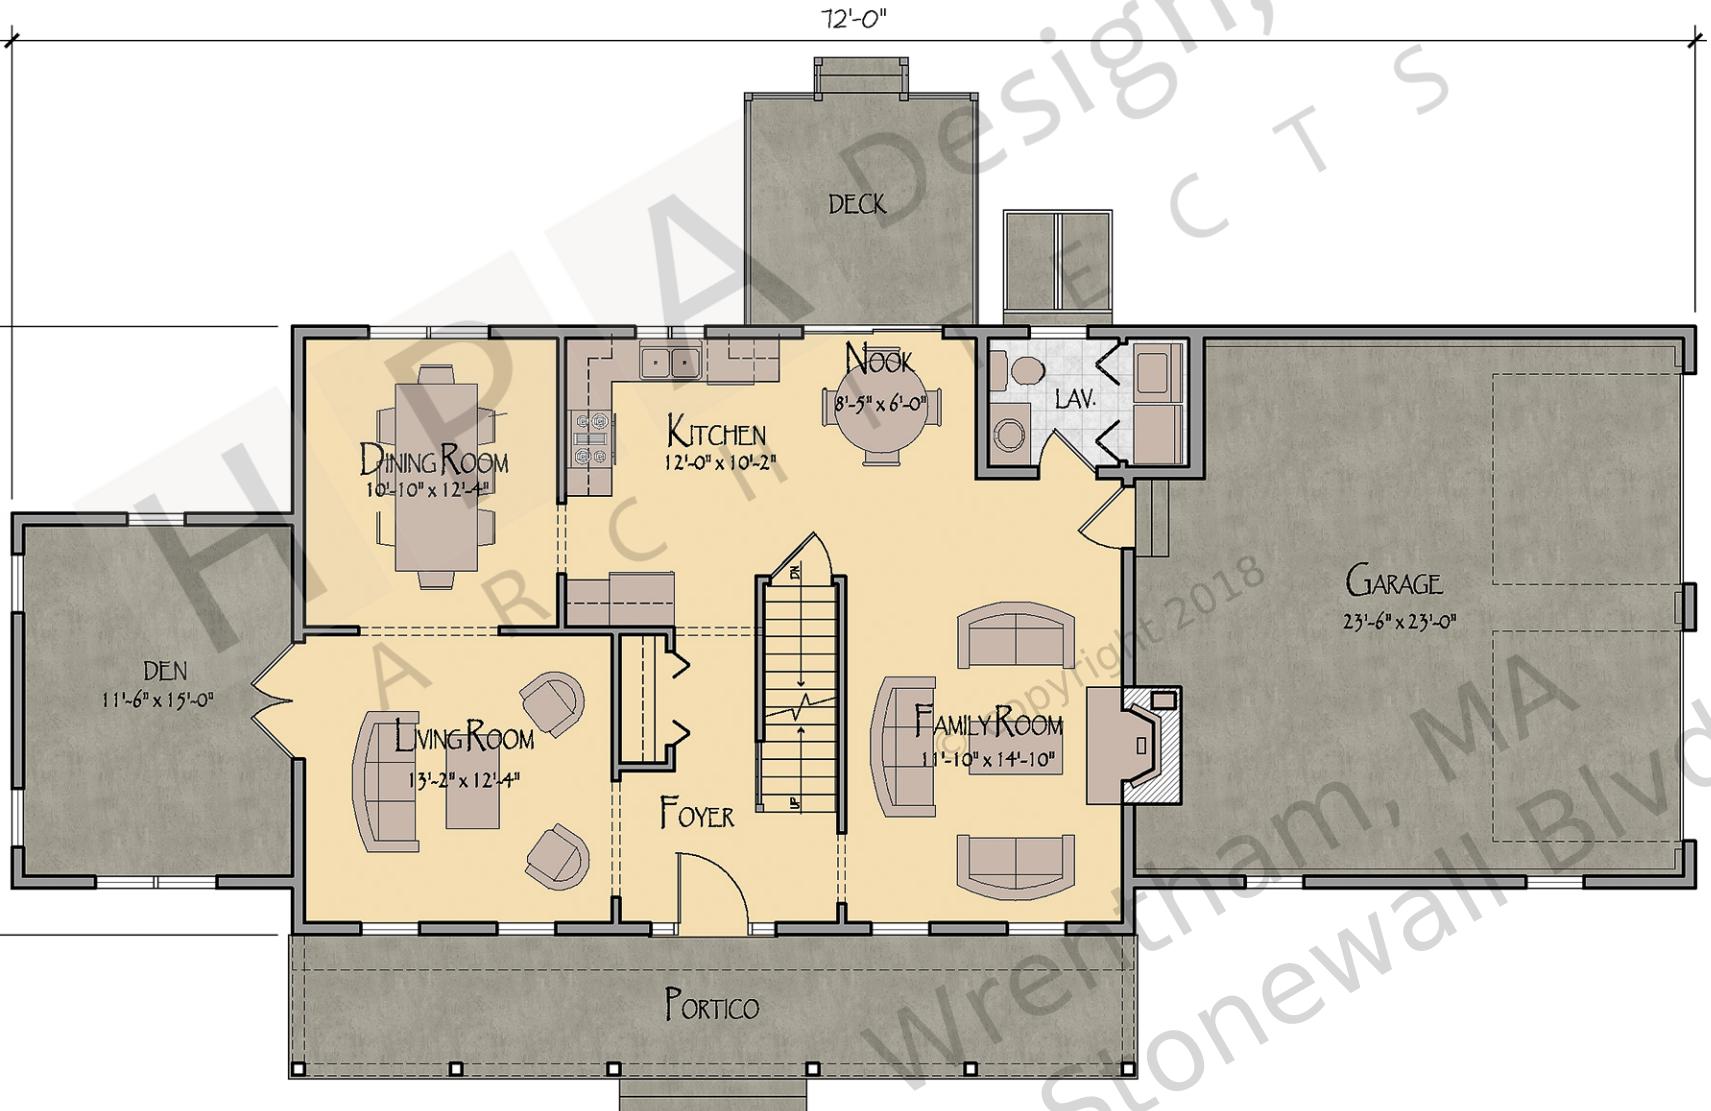

**H P A**  
Design, Inc.  
ARCHITECTS

16%  
200 Stonewall Blvd  
Wrentham, MA


**20110069**

**H P A**  
Design, Inc.  
ARCHITECTS

**H P A**

200 Stonewall Blvd  
Wrentham, MA

Rooms	9	Sq. Feet: Total	2220	Size: Width	72
Bedrooms	4	1st	1128	Depth	26
Baths: Full	2	2nd	1092		
Half	1	3rd			
Garage Size	2	Base			

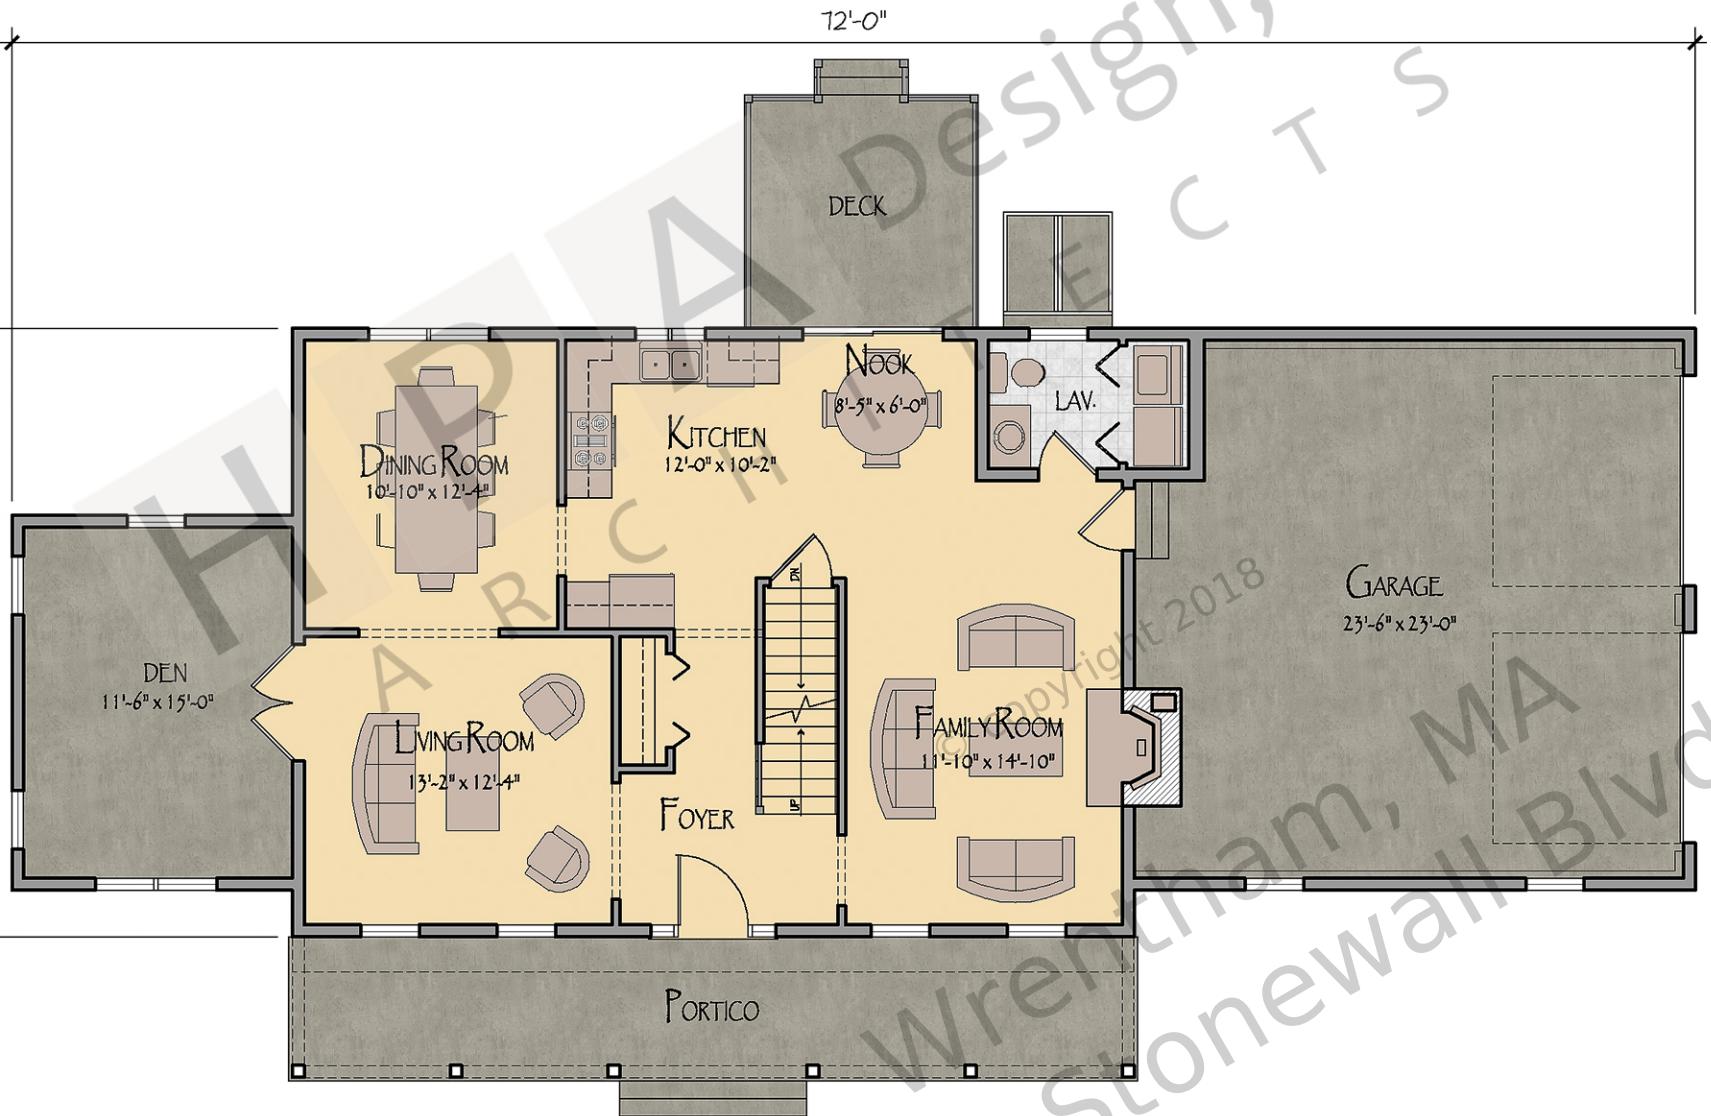

19%

**20110069**


<b>H P A</b>	Rooms 9	Sq. Feet: Total 2220	Size: Width 72
	Bedrooms 4	Depth 26	Depth 26
	Baths: Full 2		
	Half 1		
	3rd		
	Base		

Design, Inc.

200 Stonewall Blvd

Wrentham, MA

Copyright 2018

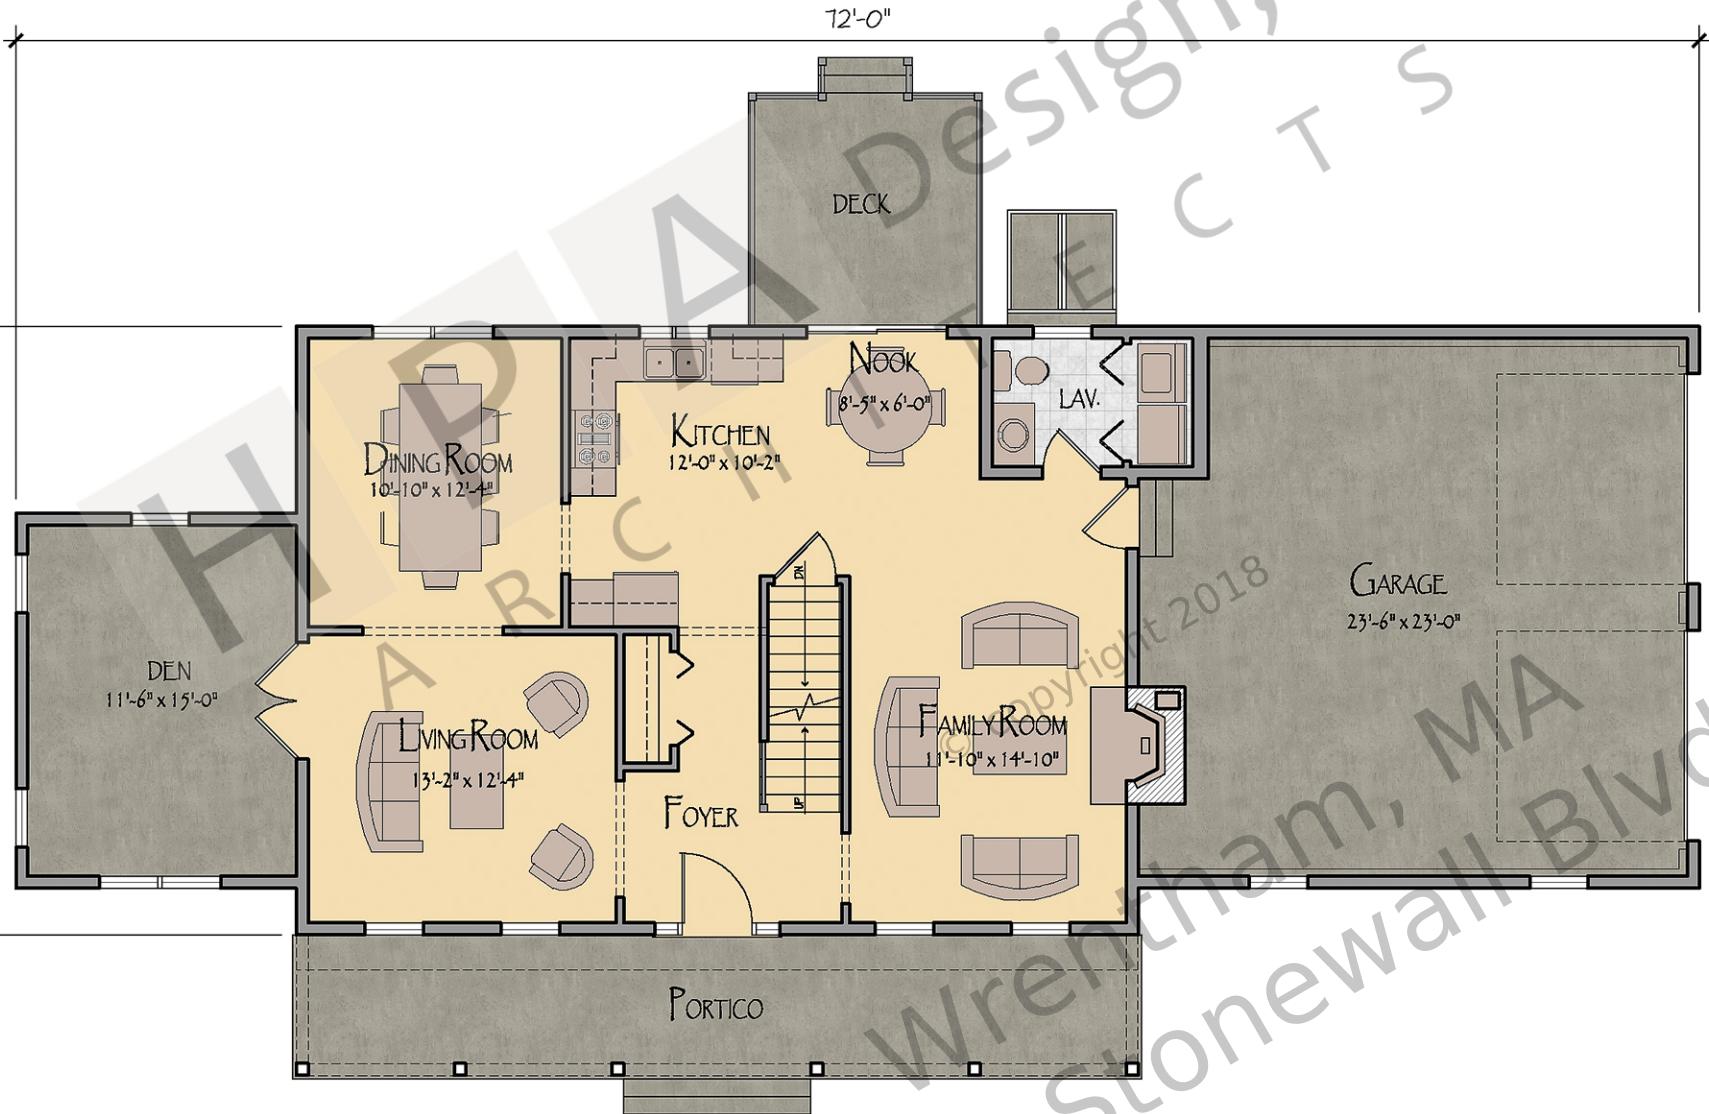

22%